





PERSPECTIVE

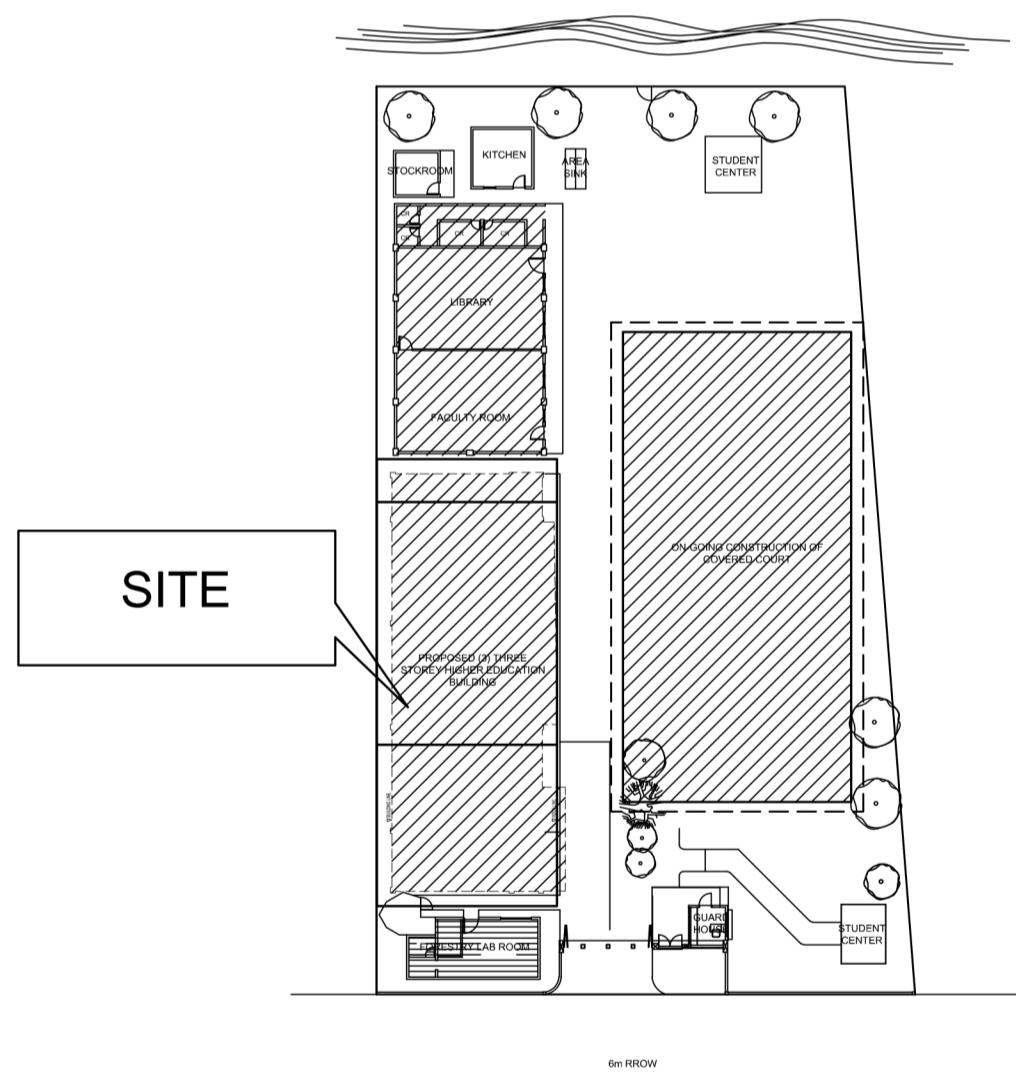

2 SITE LOCATION PLAN
A 1 SCALE N T S

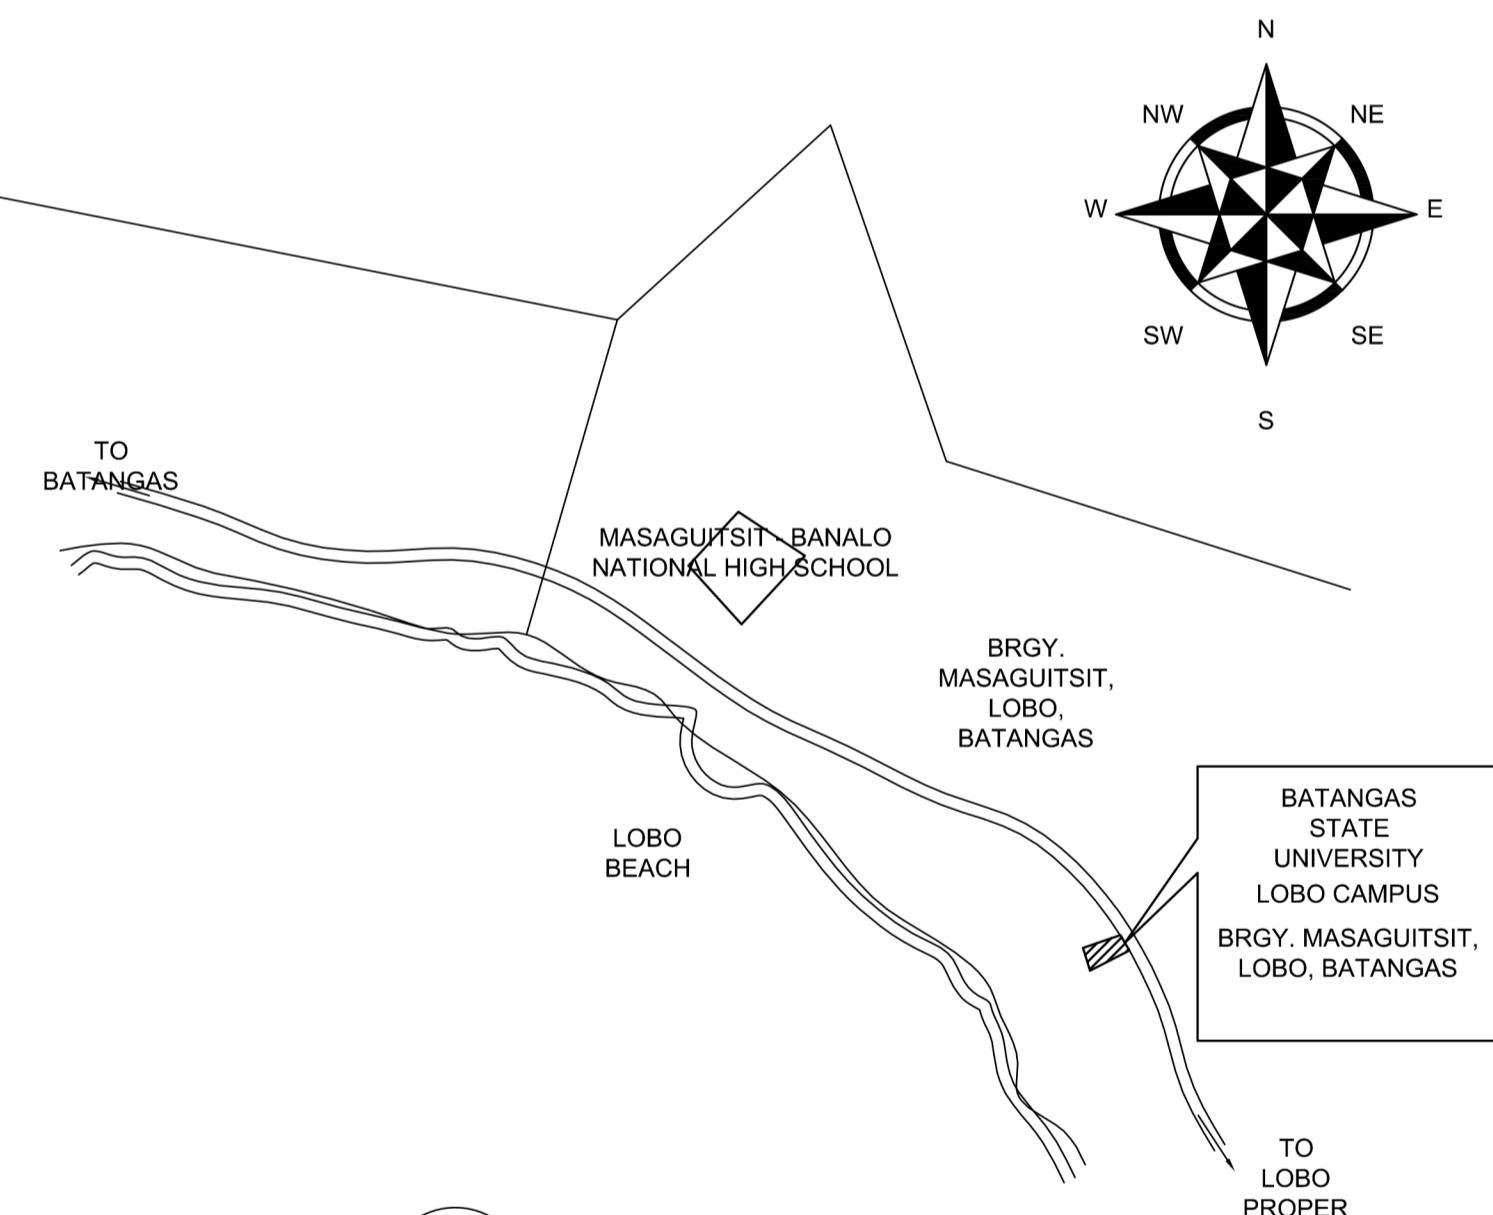

3 **VICINITY MAP**
A 1 **SCALE** **NTS**

TABLE OF CONTENTS	
ARCHITECTURAL	
A-1	PERSPECTIVE VICINITY MAP SITE LOCATION MAP
A-2	SITE DEVELOPMENT
A-3	GROUND FLOOR PLAN
A-4	SECOND FLOOR PLAN
A-5	THIRD FLOOR PLAN
A-6	FRONT ELEVATION REAR ELEVATION LEFT SIDE ELEVATION RIGHT SIDE ELEVATION
A-7	SECTION THRU "A" SECTION THRU "B" DOORS AND WINDOWS SCHEDULE
A-8	ROOF PLAN
A-9	GROUND FLOOR REFLECTED CEILING PLAN
A-10	SECOND FLOOR REFLECTED CEILING PLAN
A-11	THIRD FLOOR REFLECTED CEILING PLAN
A-12	GROUND FLOOR PATTERN LAYOUT
A-13	SECOND FLOOR PATTERN LAYOUT
A-14	THIRD FLOOR PATTERN LAYOUT
A-15	RAMP RAILING DETAILS STAIR RAILING DETAILS STAIR 1 PLAN STAIR 2 PLAN STAIR NOSING DETAILS
A-16	FEMALE TOILET DETAILS MALE TOILET DETAILS PWD TOILET DETAILS
A-17	FEMALE TOILET DETAILS MALE TOILET DETAILS
STRUCTURAL	
S-1	FOUNDATION PLAN BEAM SCHEDULE COLUMN SCHEDULE C-F, SLAB, & TIE BEAM DETAIL
S-2	2/F FRAMING PLAN 3/F FRAMING PLAN TYPICAL BEAM & LINTEL BEAM DETAIL
S-3	ROOF BEAM FRAMING LEDGE DETAIL
S-4	STAIR DETAIL STAIR FOOTING DETAIL ENTRANCE STAIR DETAIL RAMP DETAIL STAIR SECTION DETAIL
S-5	ROOF FRAMING PLAN RB-MASONRY PLAN TRUSS DETAIL
S-6	TRUSS DETAIL
ELECTRICAL	
E-1	G/F LIGHTING LAY-OUT 2/F LIGHTING LAY-OUT 3/F LIGHTING LAY-OUT
E-2	G/F EXIT AND EMERGENCY LIGHTING LAY-OUT 2/F EXIT AND EMERGENCY LIGHTING LAY-OUT 3/F EXIT AND EMERGENCY LIGHTING LAY-OUT
E-3	G/F POWER LAY-OUT 2/F POWER LAY-OUT 3/F POWER LAY-OUT
E-4	G/F TELEPHONE/DATA SYSTEM LAY-OUT 2/F TELEPHONE/DATA SYSTEM LAY-OUT 3/F TELEPHONE/DATA SYSTEM LAY-OUT TELEPHONE & DATA RISER DIAGRAM
E-5	G/F FIRE ALARM SYSTEM LAY-OUT 2/F FIRE ALARM SYSTEM LAY-OUT 3/F FIRE ALARM SYSTEM LAY-OUT FIRE ALARM SYSTEM RISER DIARAM
E-6	G/F GROUNDING SYSTEM LAY-OUT GROUNDING INSTALLATION DETAIL MAIN GROUNDING INSTALLATION DETAIL
E-7	DETAILS
E-8	SINGLE LINE DIAGRAM PULL BOX DETAIL
E-9	CONCRETE PEDESTAL DETAIL
E-10	EQUIPMENT SCHEDULE PANEL SCHEDULE
PLUMBING	
P-1	G/F TO 3/F WATER LINE LAYOUT
P-2	G/F TO 3/F WASTE/DRAINAGE LINE LAYOUT
P-3	G/F TO 3/F SANITARY LINE LAYOUT
P-4	ROOF PIPING LAYOUT
P-5	MISCELLANEOUS STANDARD DETAILS
P-6	MISCELLANEOUS STANDARD DETAILS
MECHANICAL	
M-1	G/F CEILING FAN LAYOUT G/F CEILING FAN SCHEDULE LEGEND
M-2	2/F CEILING FAN LAYOUT 2/F CEILING FAN SCHEDULE LEGEND
M-3	3/F CEILING FAN LAYOUT 3/F CEILING FAN SCHEDULE LEGEND
Republic of the Philippines	
Department of Public Works & Highways	
OFFICE OF THE BUILDING OFFICIAL	
CITY / MUNICIPALITY	
LAND USE AND ZONING	
LINE AND GRADE	
ARCHITECTURAL	
STRUCTURAL	
SANITARY / PLUMBING	