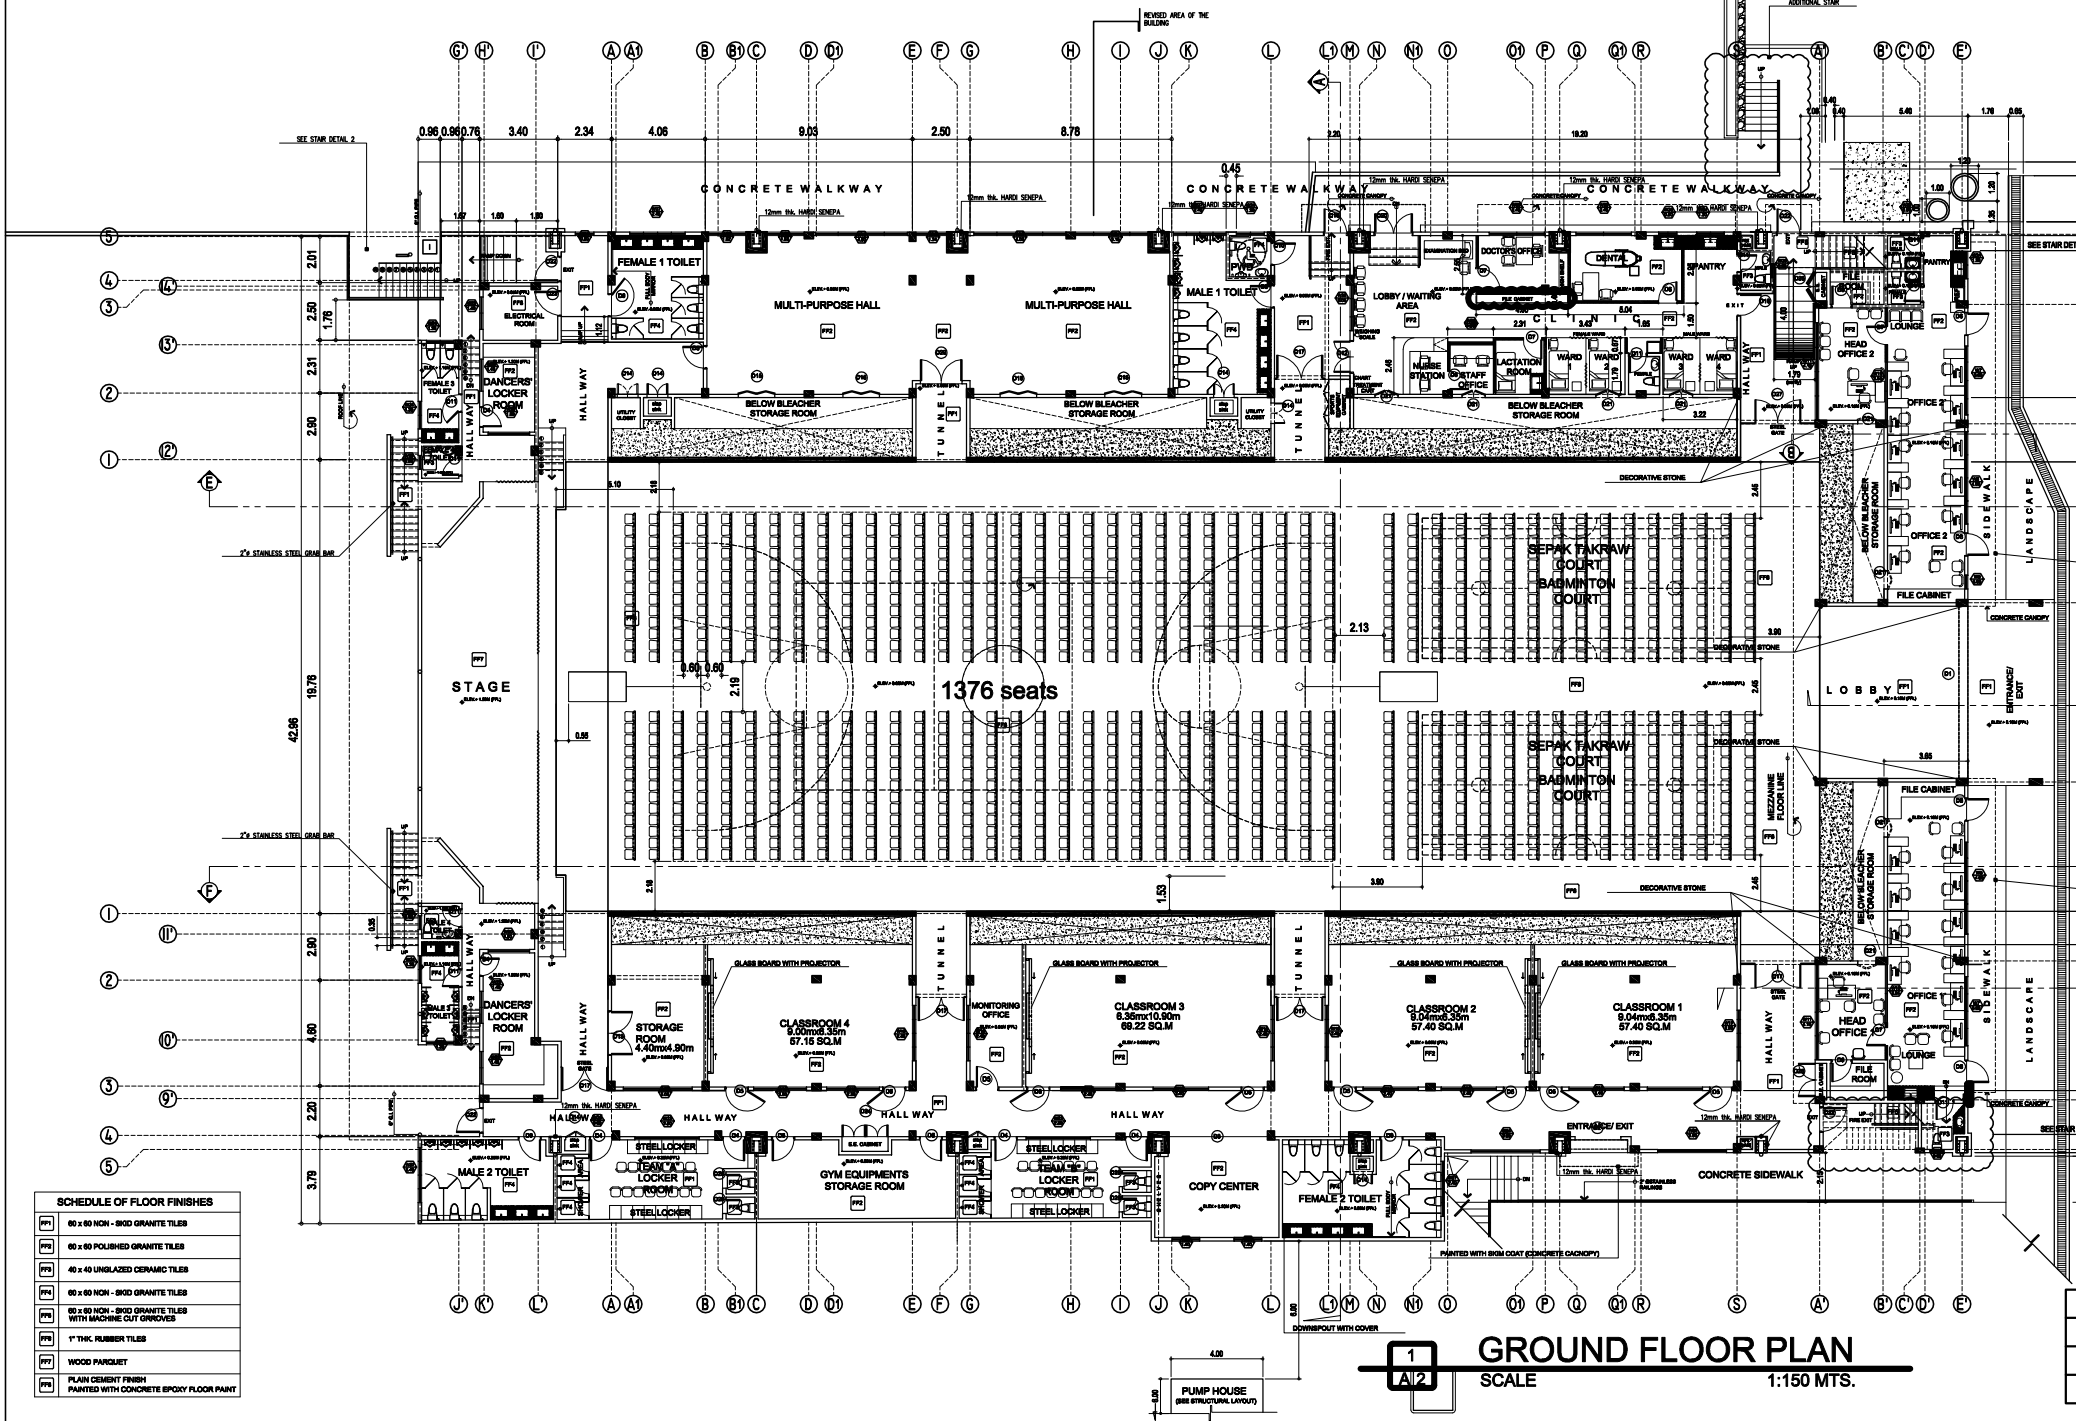

SCHEDULE OF FLOOR FINISHES	
FF1	60 x 60 NON - SKID GRANITE TILES
FF2	60 x 60 POLISHED GRANITE TILES
FF3	40 x 40 UNGLAZED CERAMIC TILES
FF4	60 x 60 NON - SKID GRANITE TILES
FF5	60 x 60 NON - SKID GRANITE TILES WITH MACHINE CUT GRROVES
FF6	1" THK. RUBBER TILES
FF7	WOOD PARQUET
FF8	PLAIN CEMENT FINISH PAINTED WITH CONCRETE EPOXY FLOOR PAINT

WALL LEGENDS:	
	SHE
	8" T
	4" T

GROUND FLOOR PLAN

1 / A2

SCALE 1:150 MTS.

BatStateU
BATANGAS STATE UNIVERSITY
Gov. Pablo Borbon Main Campus I
Rizal Avenue Extension, Batangas City
PROJECT MANAGEMENT OFFICE

ARCHITECT	SEAL	PROJECT / LOCATION:	OWNER	DESIGNED:
RODORA ROMA R. LACAP		COMPLETION OF FITNESS DEVELOPMENT CENTER	BATANGAS STATE UNIVERSITY	DRAWN/CAD:
PRC Reg No. 016034 / IAPOA No:14311-294125-082520 / TIN: 130-212-319		BATSTATEU, PABLO BORBON MAIN II Golden Country homes Alangilan Batangas City,Batangas	DR. TIRSO A. RONQUILLO UNIVERSITY PRESIDENT	CHECKED:
PTR No. 3839906 / Issued on: JANUARY 18,2021 / Issued at: Batangas City				DATE:

No.	REVISIONS	DATE	SHE
1	GROUND FLOOR PLAN	07/21/20	GR PLA