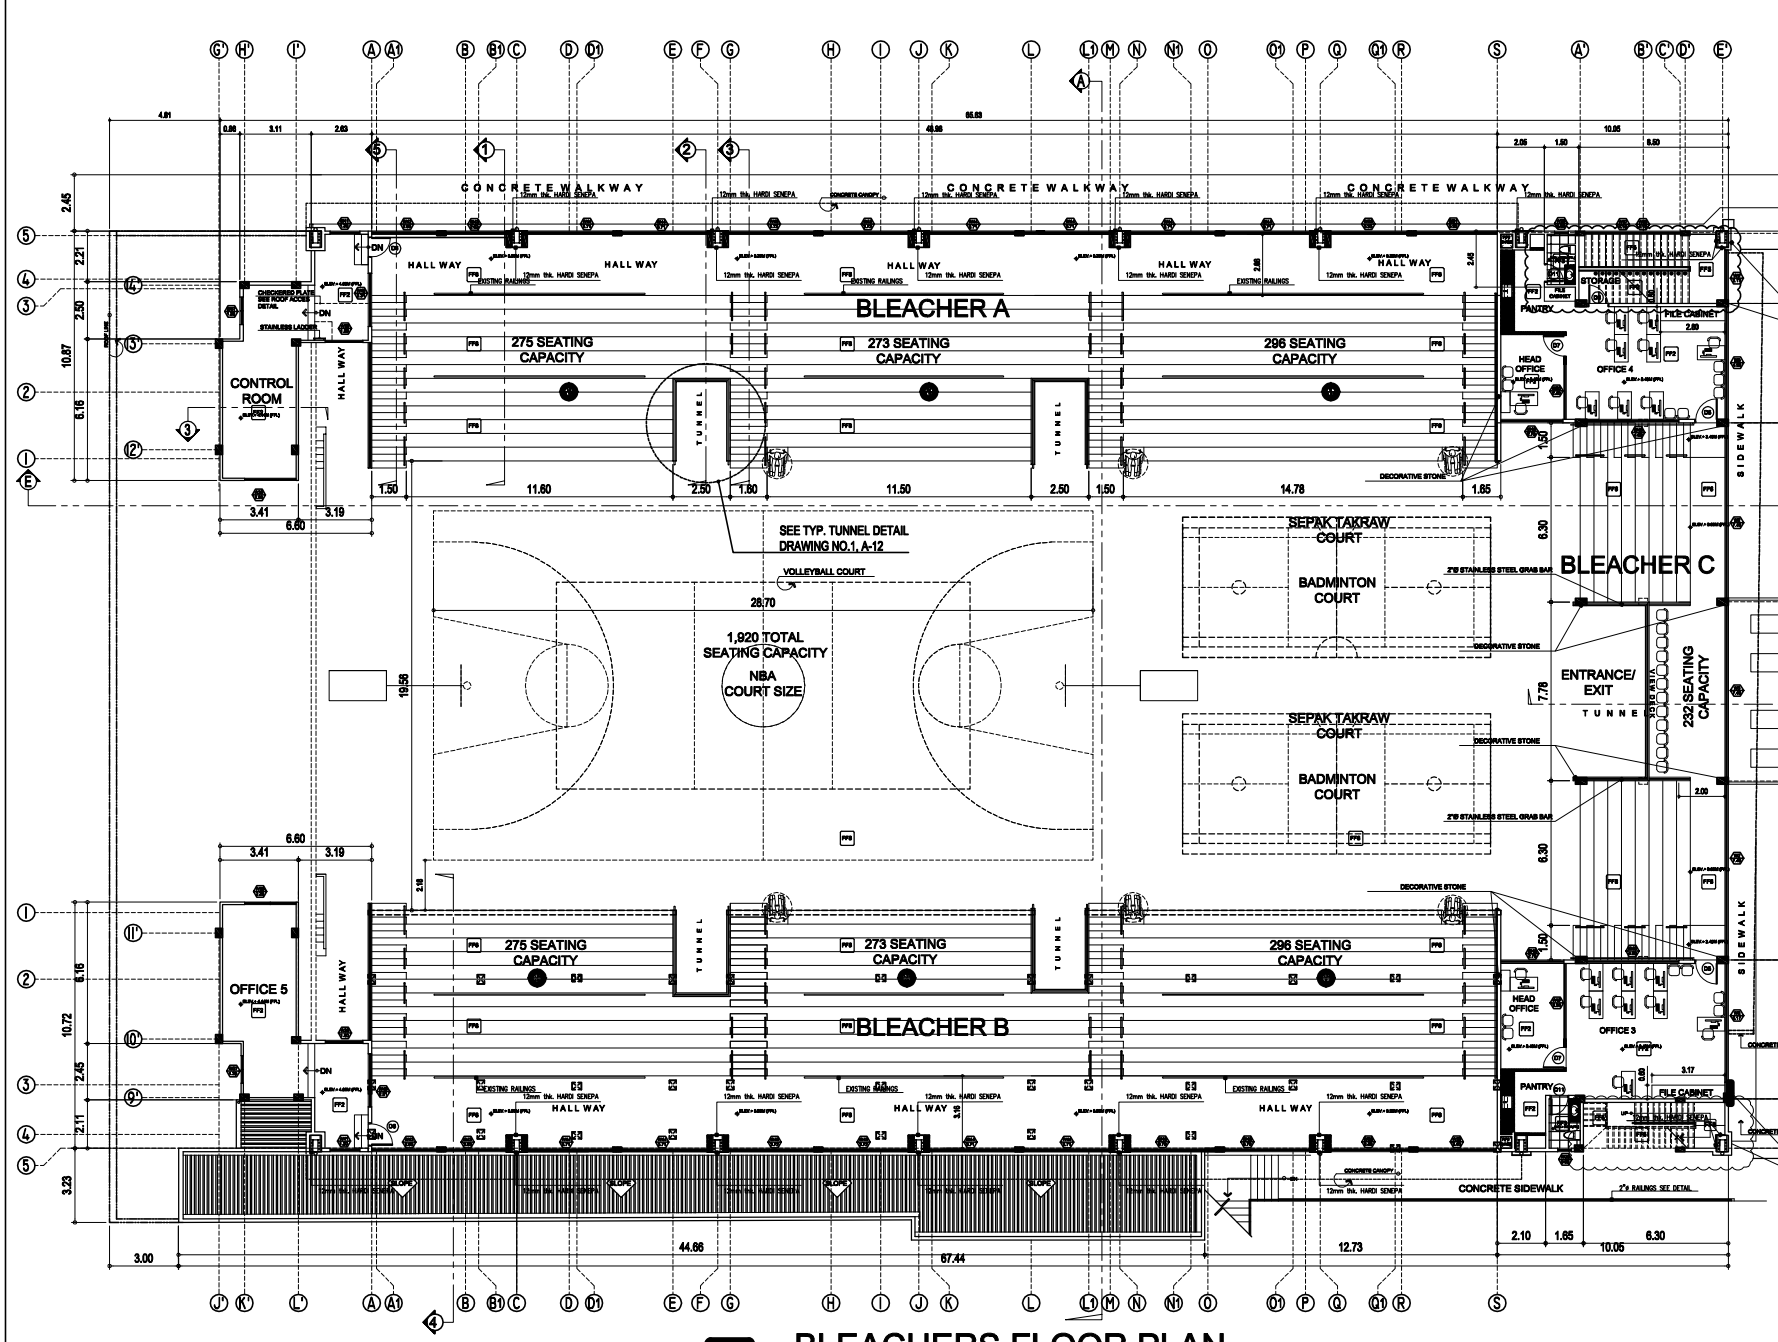

FF1	60 x 60 NON - SKID GRANITE TILES
FF2	60 x 60 POLISHED GRANITE TILES
FF3	40 x 40 UNGLAZED CERAMIC TILES
FF4	60 x 60 NON - SKID GRANITE TILES
FF5	60 x 60 NON - SKID GRANITE TILES WITH MACHINE CUT GROOVES
FF6	1" THK. RUBBER TILES
FF7	WOOD PARQUET
FF8	PLAIN CEMENT FINISH PAINTED WITH CONCRETE EPOXY FLOOR PAINT

BLEACHERS FLOOR PLAN

1 A3

SCALE 1:150 MTS.

SECOND FLOOR PL

2 A3

SCALE:

WALL LEGENDS:

	SH
	6" T
	4" T

BatStateU
BATANGAS STATE UNIVERSITY
Gov. Pablo Borbon Main Campus I
Rizal Avenue Extension, Batangas City
PROJECT MANAGEMENT OFFICE

ARCHITECT	SEAL	PROJECT / LOCATION:	OWNER	DESIGNED:
RODORA ROMA R. LACAP		COMPLETION OF FITNESS DEVELOPMENT CENTER BATSTATEU, MAIN CAMPUS II Golden Country homes Alangilan Batangas City,Batangas	BATANGAS STATE UNIVERSITY DR. TIRSO A. RONQUILLO UNIVERSITY PRESIDENT	DRAWN/CAD: CHECKED: DATE:

PRC Reg No. 016034	IAPOA No. 14311-294125-082520	TIN: 130-212-319
PTR No. 3839906	Issued on: JANUARY 18,2021	Issued at: Batangas City

No.	REVISIONS	DATE